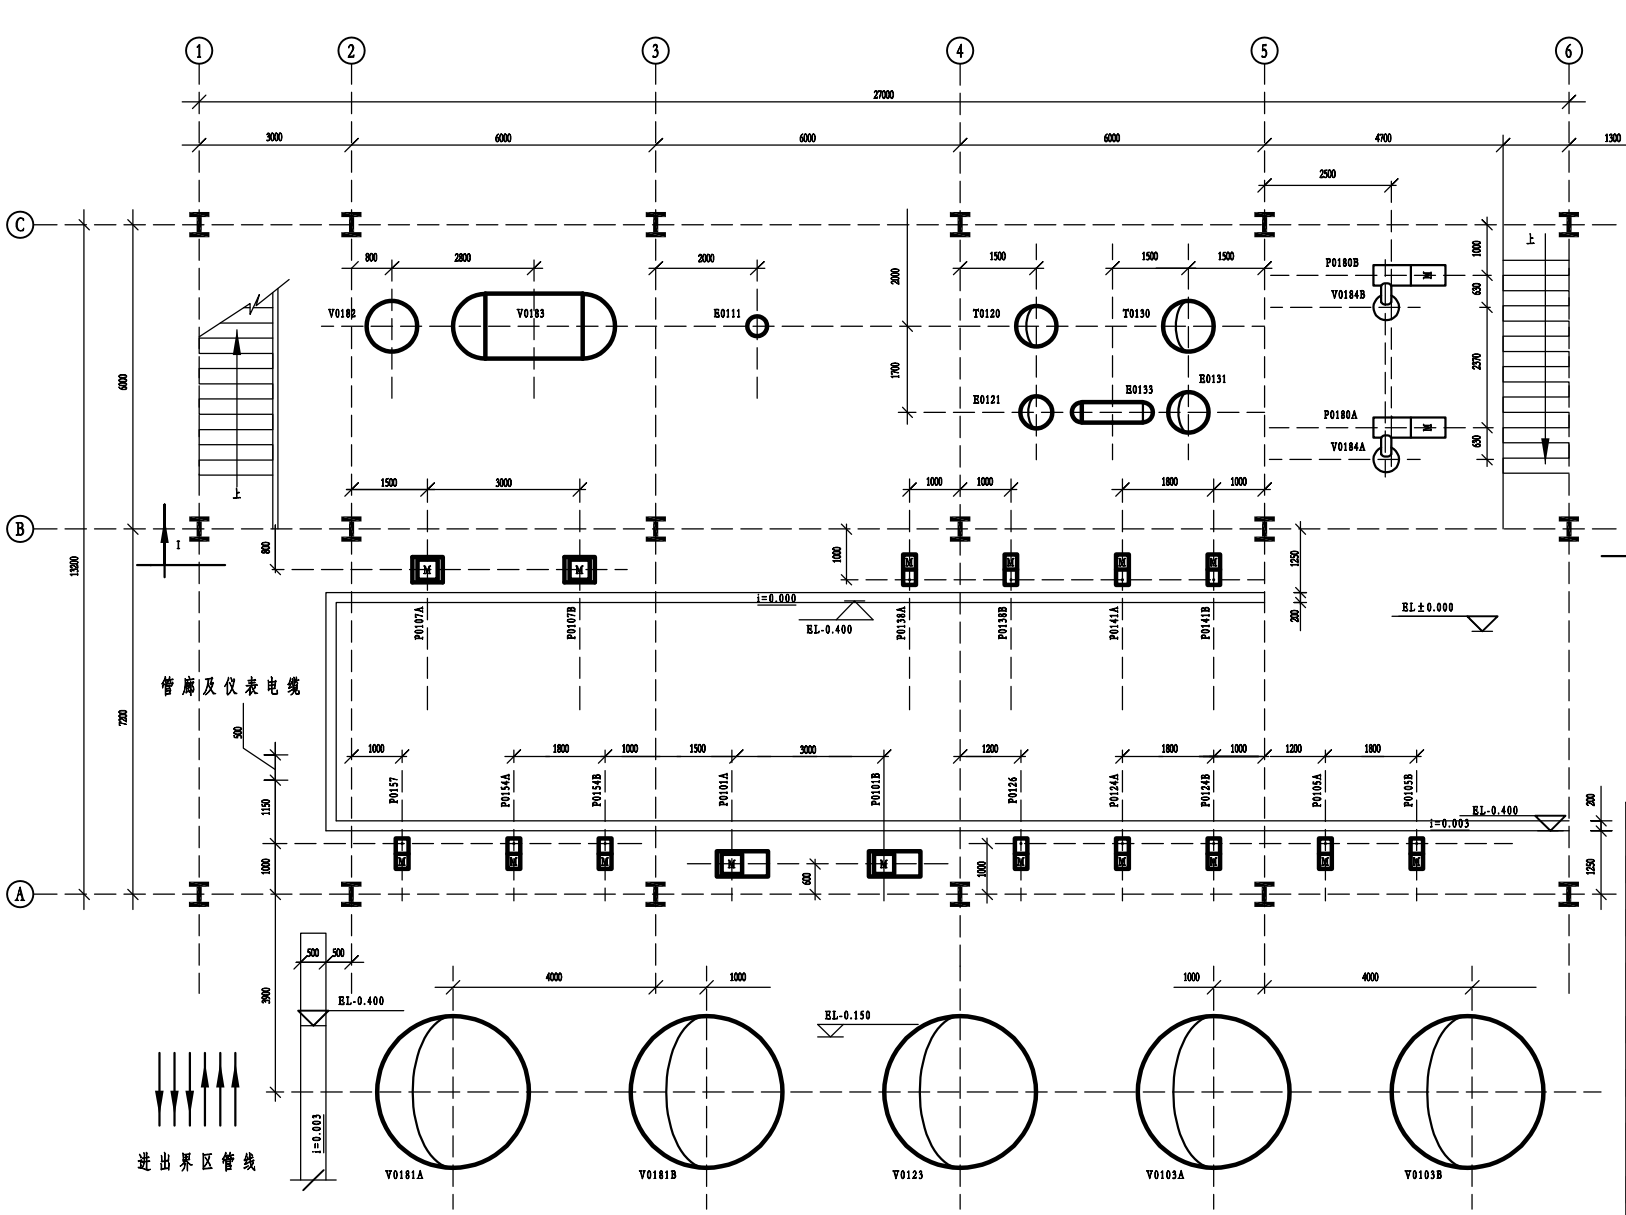


EL±0.000平面

附注说明：

1.立面图见图号XXXX-40-4-2。
2.地面设计标高EL±0.000
3.图中标高尺寸单位为m；其他尺寸单位为mm。
4.布置图中对于部分辅助小设备（如X0106、X0108）未显示。

设备位号	设备名称	数量	设备位号	设备名称	数量
V0185	×××水封	1	V0188	×××槽	1
V0183	×××罐	1	V0184	×××器	2
V0181	×××槽	2	V0182	×××罐	1
V0123	×××槽	1	V0137	×××罐	1
T0130	×××塔	1	V0103	×××贮槽	2
R0110	反应器	1	T0120	×××塔	1
P0157	×××泵	1	P0108	×××泵	2
P0141	×××泵	2	P0154	×××泵	2
P0126	×××泵	1	P0138	×××泵	2
P0107	×××泵	2	P0124	×××泵	2
P0101	×××泵	2	P0105	×××泵	2
E0132	×××换热器	1	E0133	×××换热器	1
E0122	×××换热器	1	E0131	×××换热器	1
E0112	×××换热器	1	E0121	×××换热器	1
E0104	×××换热器	1	E0111	×××换热器	1

××××工程公司				(工程名称)	
职责	签字	日期	×××设备布置图 EL±0.000平面	设计项目	
设计				设计阶段	详细工程设计
制图	钱毅扬			图号	版次
校核				××××-40-4-1	
审核					
2023年11月			比例 1:50	第 1 张	共 1 张