序号	名称	kg/h	w/%
1	乙苯	191	18
2	对二甲苯	191	18
3	间二甲苯	424	40
4	邻二甲苯	254	24
合计		1060	100

E101
二甲苯塔
(浮阀塔)
Φ=1600x52600
N=120

E101
邻苯塔
(浮阀塔)
Φ=1600x52600
N=120

E101
乙苯塔
(浮阀塔)
Φ=1600x52600
N=120

E101
乙苯冷凝器
F=100m²
Q=6280MJ

序号	名称	kg/h	w/%
1	乙苯	173.5	98.3
2	对二甲苯	1.0	0.57
3	间二甲苯	2.0	1.13
4	邻二甲苯	0	0
合计		176.5	100

序号	名称	kg/h	w/%
1	乙苯	17.5	2.0
2	对二甲苯	190	21.5
3	间二甲苯	422	47.8
4	邻二甲苯	254	28.7
合计		883.5	100

E104
乙苯冷凝器
F=3m²
Q=37MJ

E101
釜液冷凝器
F=13m²
Q=314MJ

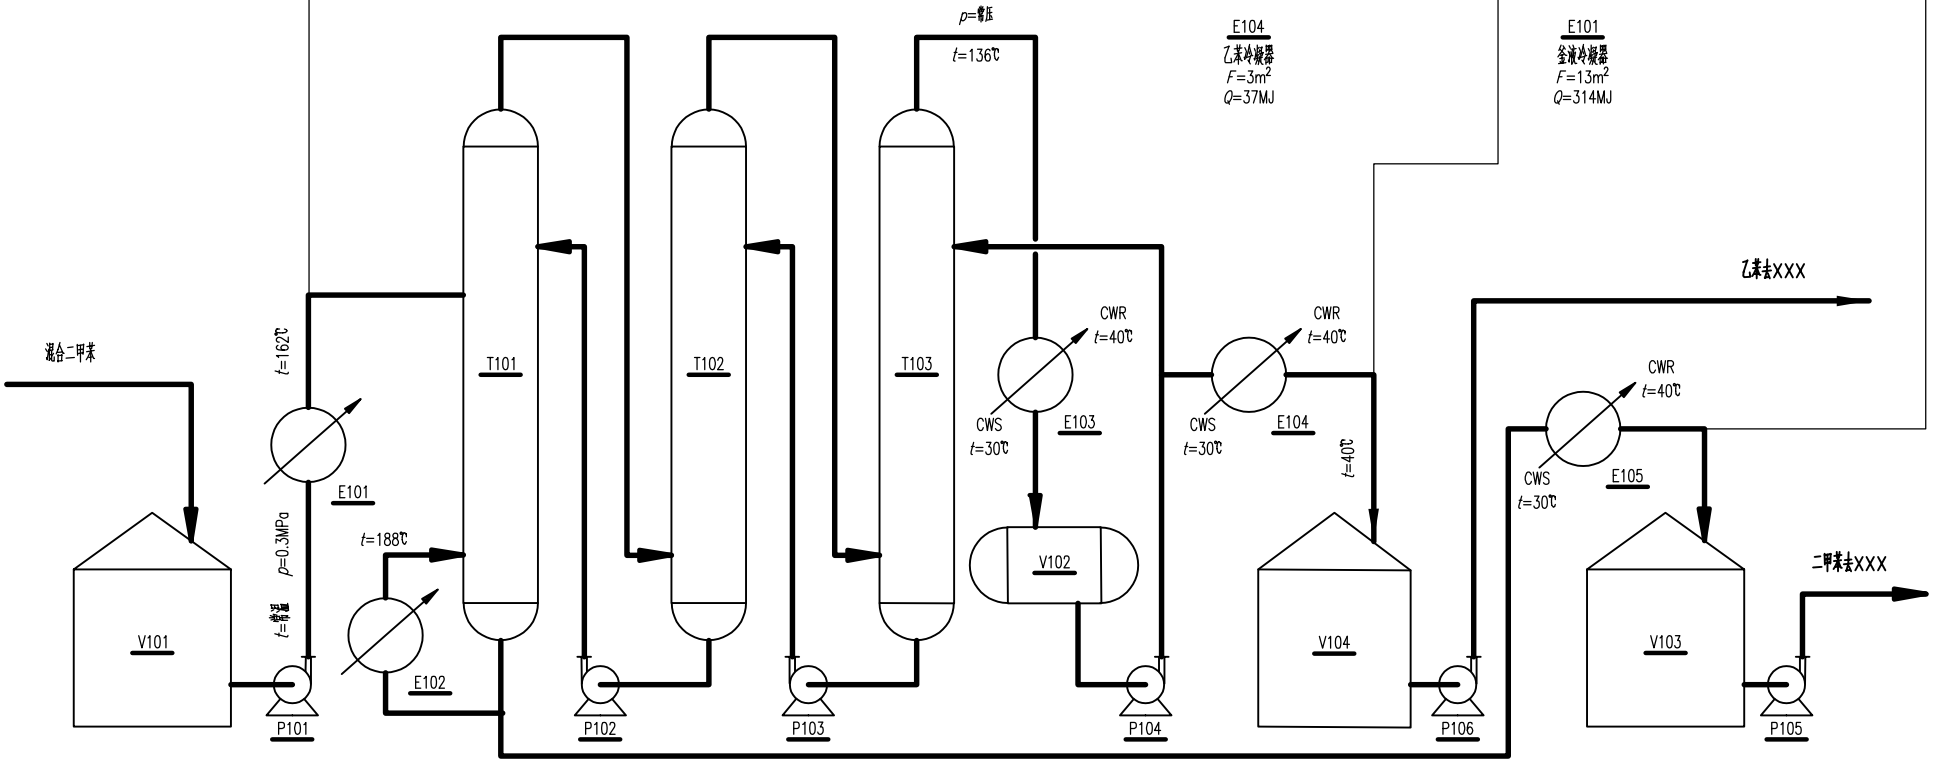

V101	混合苯储槽		
E101	预热器	F=5.7m²	Q=364MJ
E101	再沸器	F=200m²	Q=615MJ
E101	预热器		
E101	预热器		
V102	回流槽		
P104	回流泵		
P104	乙苯贮槽		
P106	乙苯泵		
P104	二甲苯贮槽		
P105	二甲苯泵		
P101	原料泵		

北京化工大学			2023年10月	化实2101班	
职责	签字	日期	C8工段物料流程图	设计项目	
设计				设计阶段	
制图					
校对					
审核					
审定			比例	专业	第1页 共1页